


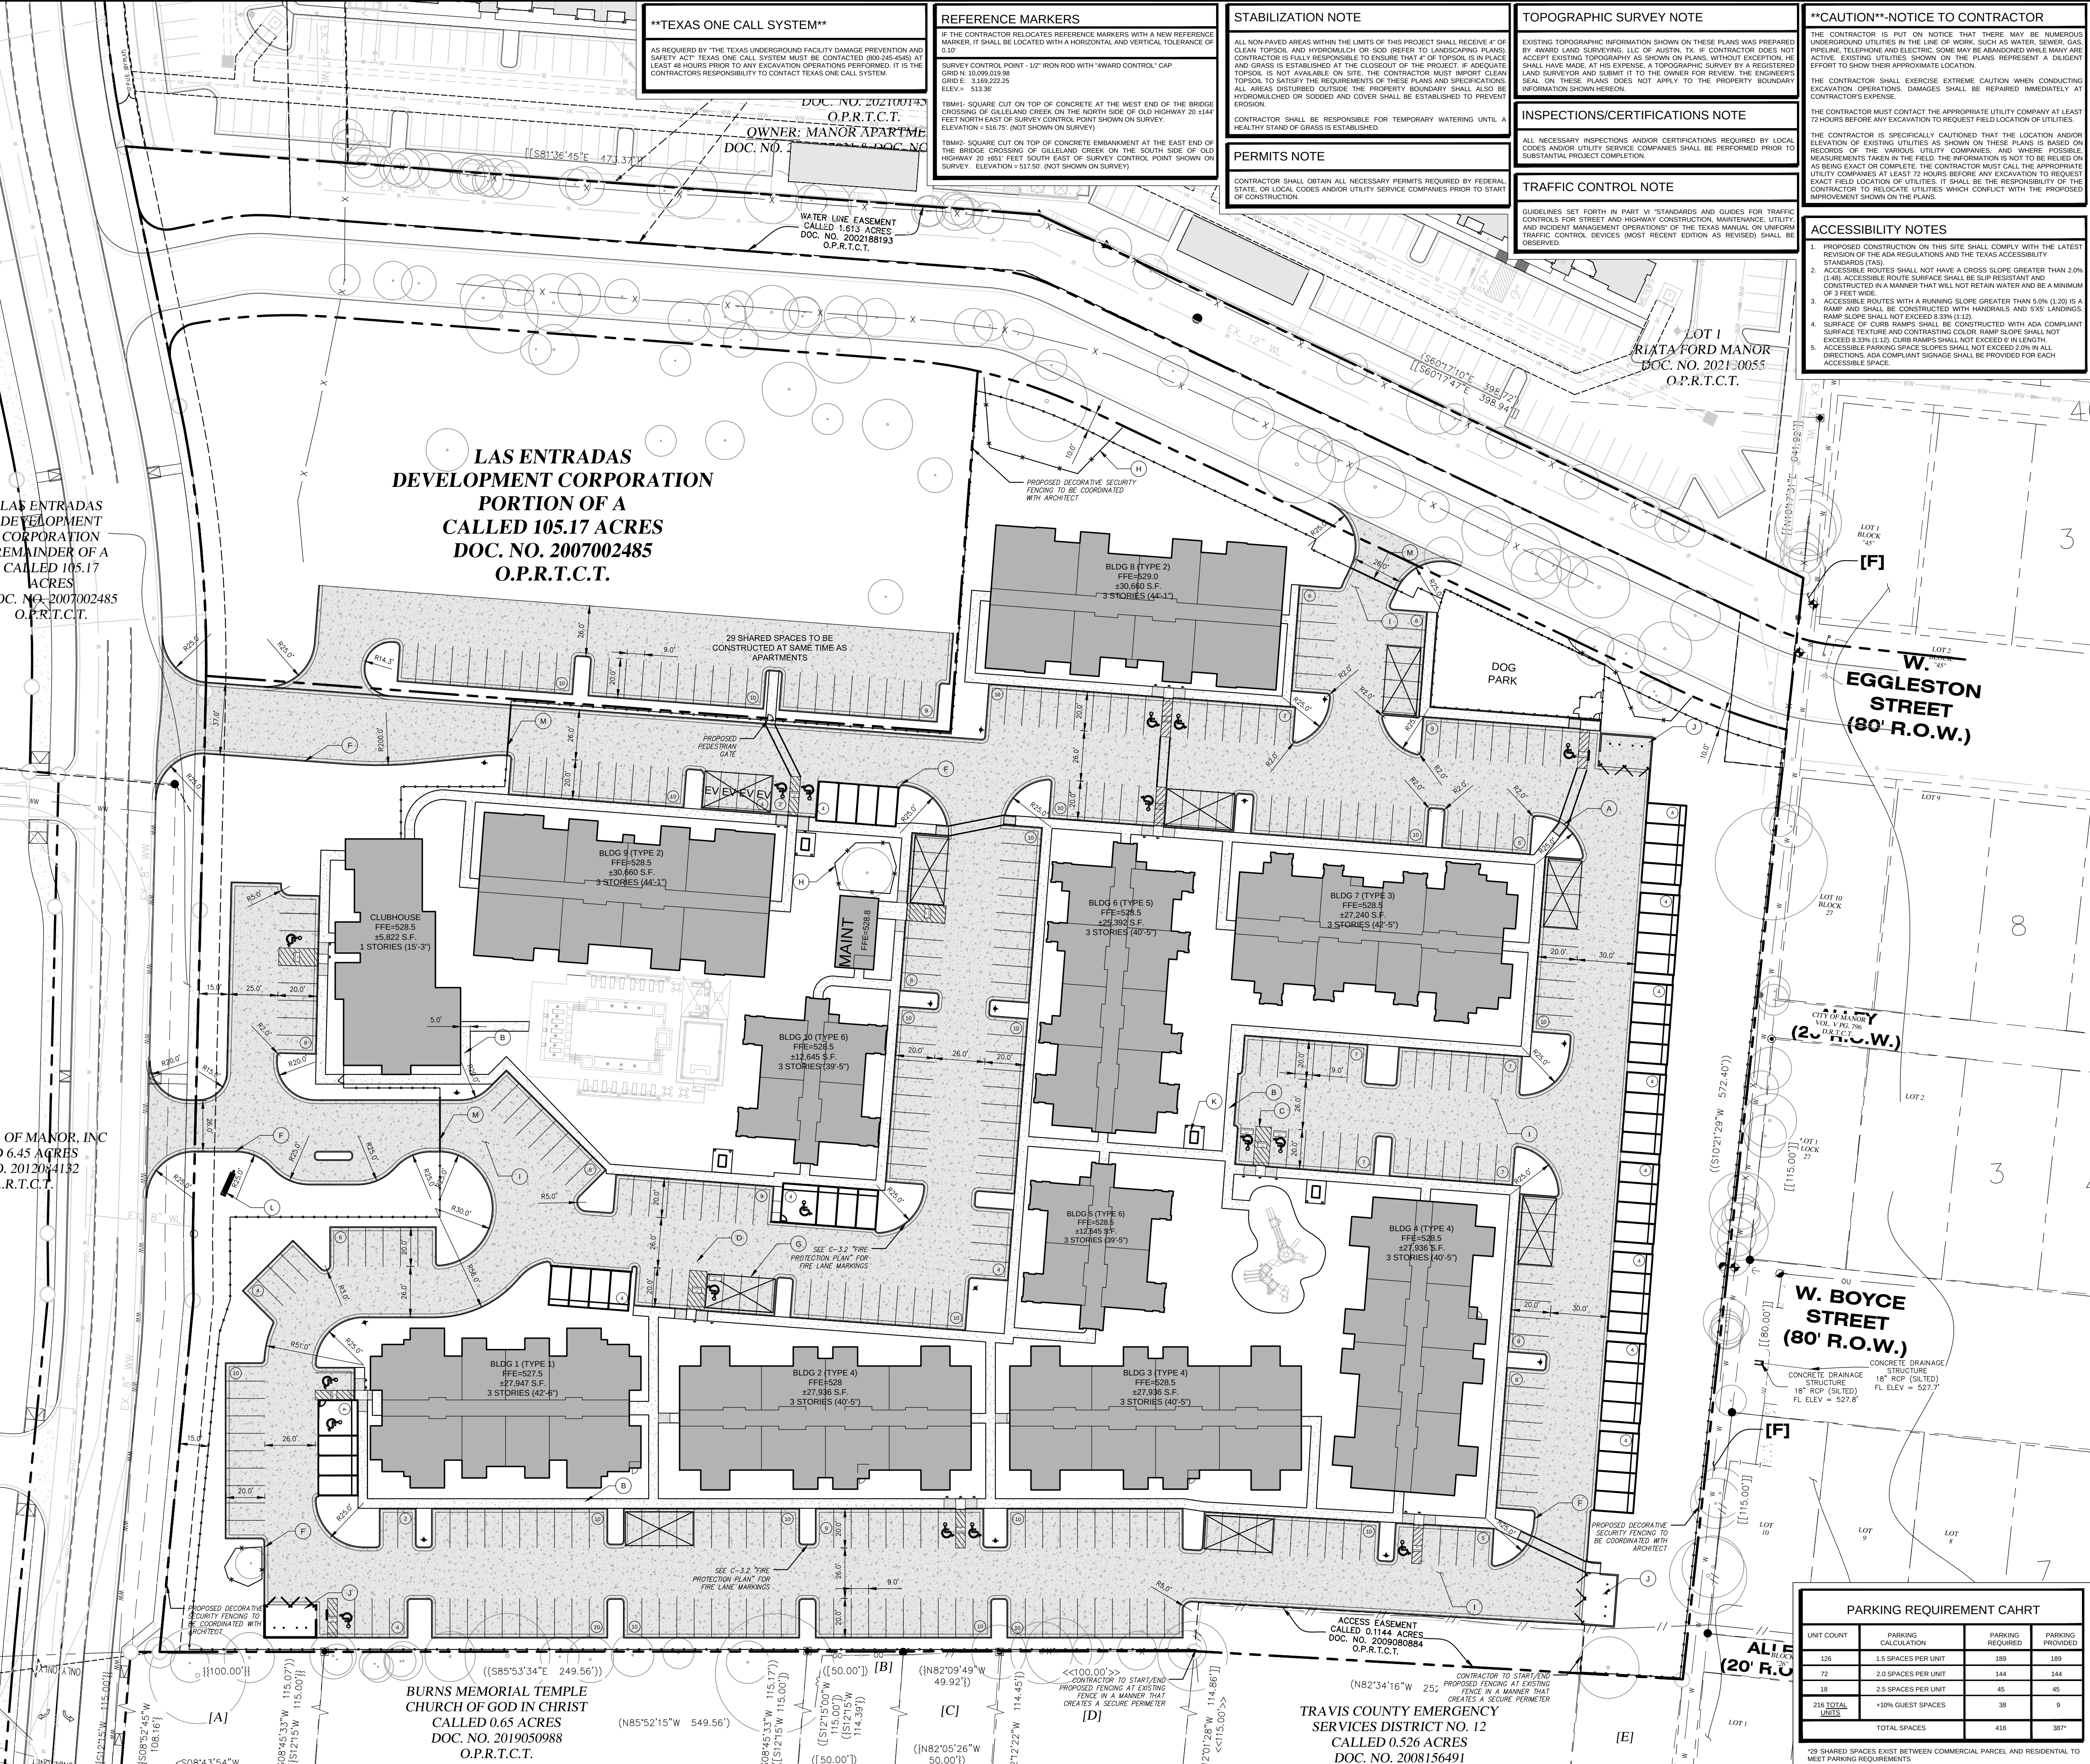

LAS ENTRADAS
DEVELOPMENT CORPORATION
REMAINDER OF A
CALLED 105.17
ACRES
DOC. NO. 2007002485
O.P.R.T.C.T.

B OF MANOR, INC
D 6.45 ACRES
O. 2012084132
P.R.T.C.T.

****TEXAS ONE CALL SYSTEM****
IF THE CONTRACTOR RELOCATES REFERENCE MARKERS WITH A NEW REFERENCE MARKER, IT SHALL BE LOCATED WITH A HORIZONTAL AND VERTICAL TOLERANCE OF 0.10'.
SURVEY CONTROL POINT - 12" IRON ROD WITH "WARD CONTROL" CAP
GRID N 10.099.013.98
GRID E 3.169.222.25
ELEV = 513.36'
TBM#1: SQUARE CUT ON TOP OF CONCRETE AT THE WEST END OF THE BRIDGE CROSSING OF GILLENDALE CREEK ON THE NORTH SIDE OF OLD HIGHWAY 20 134' FEET NORTH EAST OF SURVEY CONTROL POINT SHOWN ON SURVEY. ELEVATION = 518.75' (NOT SHOWN ON SURVEY).
TBM#2: SQUARE CUT ON TOP OF CONCRETE EMANKMENT AT THE EAST END OF THE BRIDGE CROSSING OF GILLENDALE CREEK ON THE SOUTH SIDE OF OLD HIGHWAY 20 162' FEET SOUTH EAST OF SURVEY CONTROL POINT SHOWN ON SURVEY. ELEVATION = 517.50' (NOT SHOWN ON SURVEY).
OWNER: MANOR APARTME
DOC. NO. 2021001913
O.P.R.T.C.T.
WATER LINE EASEMENT
CALLED 1.515 ACRES
DOC. NO. 2002188183
O.P.R.T.C.T.

REFERENCE MARKERS
IF THE CONTRACTOR RELOCATES REFERENCE MARKERS WITH A NEW REFERENCE MARKER, IT SHALL BE LOCATED WITH A HORIZONTAL AND VERTICAL TOLERANCE OF 0.10'.
SURVEY CONTROL POINT - 12" IRON ROD WITH "WARD CONTROL" CAP
GRID N 10.099.013.98
GRID E 3.169.222.25
ELEV = 513.36'
TBM#1: SQUARE CUT ON TOP OF CONCRETE AT THE WEST END OF THE BRIDGE CROSSING OF GILLENDALE CREEK ON THE NORTH SIDE OF OLD HIGHWAY 20 134' FEET NORTH EAST OF SURVEY CONTROL POINT SHOWN ON SURVEY. ELEVATION = 518.75' (NOT SHOWN ON SURVEY).
TBM#2: SQUARE CUT ON TOP OF CONCRETE EMANKMENT AT THE EAST END OF THE BRIDGE CROSSING OF GILLENDALE CREEK ON THE SOUTH SIDE OF OLD HIGHWAY 20 162' FEET SOUTH EAST OF SURVEY CONTROL POINT SHOWN ON SURVEY. ELEVATION = 517.50' (NOT SHOWN ON SURVEY).

STABILIZATION NOTE
ALL NON-PAVED AREAS WITHIN THE LIMITS OF THIS PROJECT SHALL RECEIVE 4" OF CLEAN TOPSOIL AND HYDROMULCH OR SOD (REFER TO LANDSCAPING PLANS). CONTRACTOR IS FULLY RESPONSIBLE TO ENSURE THAT 4" OF TOPSOIL IS IN PLACE AND GRASS IS ESTABLISHED AT THE CLOSEOUT OF THE PROJECT. IF ADEQUATE TOPSOIL IS NOT AVAILABLE ON SITE, THE CONTRACTOR MUST IMPORT CLEAN TOPSOIL TO SATISFY THE REQUIREMENTS OF THESE PLANS AND SPECIFICATIONS. ALL AREAS DISTURBED OUTSIDE THE PROPERTY BOUNDARY SHALL ALSO BE HYDROMULCHED OR SODDED AND COVER SHALL BE ESTABLISHED TO PREVENT EROSION.
CONTRACTOR SHALL BE RESPONSIBLE FOR TEMPORARY WATERING UNTIL A HEALTHY STAND OF GRASS IS ESTABLISHED.

PERMITS NOTE
CONTRACTOR SHALL OBTAIN ALL NECESSARY PERMITS REQUIRED BY FEDERAL, STATE, OR LOCAL CODES AND/OR UTILITY SERVICE COMPANIES PRIOR TO START OF CONSTRUCTION.

TOPOGRAPHIC SURVEY NOTE
EXISTING TOPOGRAPHIC INFORMATION SHOWN ON THESE PLANS WAS PREPARED BY 4WARD LAND SURVEYING, L.L.C. OF AUSTIN, TX. IF CONTRACTOR DOES NOT ACCEPT EXISTING TOPOGRAPHY AS SHOWN ON PLANS, WITHOUT EXCEPTION, HE SHALL HAVE MADE, AT HIS EXPENSE, A TOPOGRAPHIC SURVEY BY A REGISTERED LAND SURVEYOR AND SUBMIT IT TO THE OWNER FOR REVIEW. THE ENGINEER'S SEAL ON THESE PLANS DOES NOT APPLY TO THE PROPERTY BOUNDARY INFORMATION SHOWN HEREON.

INSPECTIONS/CERTIFICATIONS NOTE
ALL NECESSARY INSPECTIONS AND/OR CERTIFICATIONS REQUIRED BY LOCAL CODES AND/OR UTILITY SERVICE COMPANIES SHALL BE PERFORMED PRIOR TO SUBSTANTIAL PROJECT COMPLETION.

TRAFFIC CONTROL NOTE
GUIDELINES SET FORTH IN PART VI "STANDARDS AND GUIDES FOR TRAFFIC CONTROLS FOR STREET AND HIGHWAY CONSTRUCTION, MAINTENANCE, UTILITY AND INCIDENT MANAGEMENT OPERATIONS" OF THE TEXAS MANUAL ON UNIFORM TRAFFIC CONTROL DEVICES (MOST RECENT EDITION AS REVISED) SHALL BE OBSERVED.

****CAUTION** - NOTICE TO CONTRACTOR**
THE CONTRACTOR IS PUT ON NOTICE THAT THERE MAY BE NUMEROUS UNDERGROUND UTILITIES IN THE LINE OF WORK, SUCH AS WATER, SEWER, GAS, PIPELINE, TELEPHONE AND ELECTRIC, SOME MAY BE ABANDONED WHILE MANY ARE ACTIVE. EXISTING UTILITIES SHOWN ON THE PLANS REPRESENT A DILIGENT EFFORT TO SHOW THEIR APPROXIMATE LOCATION.
THE CONTRACTOR SHALL EXERCISE EXTREME CAUTION WHEN CONDUCTING EXCAVATION OPERATIONS. DAMAGES SHALL BE REPAIRED IMMEDIATELY AT CONTRACTOR'S EXPENSE.
THE CONTRACTOR MUST CONTACT THE APPROPRIATE UTILITY COMPANY AT LEAST 72 HOURS BEFORE ANY EXCAVATION TO REQUEST FIELD LOCATION OF UTILITIES.
THE CONTRACTOR IS SPECIFICALLY CAUTIONED THAT THE LOCATION AND/OR ELEVATION OF EXISTING UTILITIES AS SHOWN ON THESE PLANS IS BASED ON RECORDS OF THE VARIOUS UTILITY COMPANIES, AND WHERE POSSIBLE, MEASUREMENTS TAKEN IN THE FIELD. THE INFORMATION IS NOT TO BE RELIED ON AS BEING EXACT OR COMPLETE. THE CONTRACTOR MUST CALL THE APPROPRIATE UTILITY COMPANIES AT LEAST 72 HOURS BEFORE ANY EXCAVATION TO REQUEST EXACT FIELD LOCATION OF UTILITIES. IT SHALL BE THE RESPONSIBILITY OF THE CONTRACTOR TO RELOCATE UTILITIES WHICH CONFLICT WITH THE PROPOSED IMPROVEMENTS SHOWN ON THE PLANS.

ACCESSIBILITY NOTES
1. PROPOSED CONSTRUCTION ON THIS SITE SHALL COMPLY WITH THE LATEST REVISION OF THE ADA REGULATIONS AND THE TEXAS ACCESSIBILITY STANDARDS (TAS).
2. ACCESSIBLE ROUTES SHALL NOT HAVE A CROSS SLOPE GREATER THAN 2.0% (2:100). ACCESSIBLE ROUTE SURFACE SHALL BE SLIP RESISTANT AND CONSTRUCTED IN A MANNER THAT WILL NOT RETAIN WATER AND BE A MINIMUM OF 3 FEET WIDE.
3. ACCESSIBLE ROUTES WITH A RUNNING SLOPE GREATER THAN 5.0% (1:20) IS A RAMP AND SHALL BE CONSTRUCTED WITH HANDRAILS AND 5X5' LANDINGS. RAMP SLOPE SHALL NOT EXCEED 8.33% (1:12).
4. SURFACE OF CURB RAMP SHALL BE CONSTRUCTED WITH ADA COMPLIANT SURFACE TEXTURE AND CONTRASTING COLOR. RAMP SLOPE SHALL NOT EXCEED 8.33% (1:12). CURB RAMP SHALL NOT EXCEED 6' IN LENGTH.
5. ACCESSIBLE PARKING SPACE SLOPES SHALL NOT EXCEED 2.0% IN ALL DIRECTIONS. ADA COMPLIANT SIGNAGE SHALL BE PROVIDED FOR EACH ACCESSIBLE SPACE.

SITE INFORMATION

OWNER/DEVELOPER: MANOR MF LLC
178 FIRSTFIELD ROAD SUITE 203
GAITHERSBURG MO 20878

LEGAL DESCRIPTION: BEING 13.2177 ACRES OF LAND SITUATED IN THE JAMES MANOR SURVEY NO. 40, ABSTION NO. 546, TRAVIS COUNTY, TEXAS; BEING A PORTION OF THAT CERTAIN CALL 105.170 ACRE TRACT OF LAND AS DESCRIBED IN WARRANTY DEED WITH VENDOR'S LIEN TO LAS ENTRADAS DEVELOPMENT CORPORATION AND RECORDED IN DOCUMENT NO. 2007002485, OF THE OFFICIAL PUBLIC RECORDS OF TRAVIS COUNTY, TEXAS.

SITE ADDRESS: TBD

ZONED: MF-2 (MULTI-FAMILY 2S)

SETBACKS: FRONT - 20'
SIDE - 80' (3 STORY), 25' (1 STORY), 50' (2 STORY)
REAR - 80' (3 STORY), 25' (1 STORY), 50' (2 STORY)

LEGEND

NOTE: NOTE: ALL BUILDING UTILITY CONNECTION SIZE AND LOCATIONS TO BE CONFIRMED WITH ARCHITECTURAL PLANS

	WATER VALVE
	FIRE HYDRANT
	SEWER MANHOLE
	SANITARY CLEANOUT
	NUMBER OF PARKING SPACES PER ROW
	STORM SEWER
	WATER LINE
	SANITARY SEWER
	PROPOSED CURB AND GUTTER

- KEYED NOTES**
- (A) ADA CURB RAMP/SIDEWALK
 - (B) CONCRETE SIDEWALK, WIDTH PER PLAN
 - (C) ACCESSIBLE PARKING SPACE (AS SHOWN BELOW)
 - (D) ACCESSIBLE PARKING SPACE WITH BOLLARD, SIGN, STRIPING, AND SYMBOL (SEE DETAILS)
 - (E) 6" WHITE THERMOPLASTIC CROSSWALK STRIPING
 - (F) 6" WIDE FIRE LANE STRIPING PAINTED TRAFFIC RED WITH "NO PARKING - FIRE LANE" PAINTED WHITE 4" HIGH WHITE LETTERING AT 25' O.C. SEE DETAIL SHEET. NOTE - STRIPING SHOWN OFFSET FOR CLARITY.
 - (G) 6" CURB AND GUTTER
 - (H) CARPORT (DETAILS BY ARCHITECT)
 - (I) TREE PROTECTION FENCING
 - (J) CONCRETE PAVEMENT
 - (K) DUMPSTER ENCLOSURE
 - (L) TRANSFORMER AND CONCRETE PAD
 - (M) SITE MONUMENT SIGN
 - (N) SITE SECURITY FENCING & ACCESS GATES

GENERAL NOTES

- ALL WORK AND MATERIALS SHALL COMPLY WITH ALL CITY, COUNTY, STATE, FEDERAL AND OSHA REGULATIONS.
- CONTRACTOR SHALL REFER TO THE ARCHITECTURAL PLANS FOR EXACT LOCATIONS AND DIMENSIONS OF SLOPED PAVING, RMPAS, SIDEWALKS, EXIT PORCHES, PRECISE BUILDING DIMENSIONS, EXACT BUILDING UTILITY ENTRANCE LOCATIONS, TOTAL NUMBER, LOCATION, AND SIZE OF DOWNSPOUTS AND ANY OTHER APPURTENANCES WHICH ARE CONNECTED TO THE BUILDING.
- ALL DIMENSIONS AND RADI ARE TO THE FRONT OF CURB, CENTER OR END OF STRIPE, FACE OF BUILDING, OR EDGE OF PAVEMENT, UNLESS OTHERWISE NOTED.
- CONTRACTOR IS REQUIRED TO REMOVE OR RELOCATE, IN A PROPER MANNER, EXISTING IMPROVEMENTS/NATURAL FEATURES TO ALLOW FOR CONSTRUCTION OF PROPOSED IMPROVEMENTS INDICATED ON THE PLANS. ALL WORK SHALL BE IN ACCORDANCE WITH GOVERNING AUTHORITIES SPECIFICATIONS AND SHALL BE APPROVED BY SUCH. NO SEPARATE PAY FOR THIS WORK.
- CONTRACTOR IS RESPONSIBLE FOR PROTECTION AND REPLACEMENT OF ALL PROPERTY CORNERS. PROPERTY CORNERS DAMAGED BY CONTRACTOR SHALL BE REPLACED BY A REGISTERED PROFESSIONAL LAND SURVEYOR AT CONTRACTOR'S EXPENSE.
- CONTRACTOR SHALL BE RESPONSIBLE FOR DOCUMENTING ALL EXISTING DAMAGE AND NOTIFY OWNER AND/OR ENGINEER PRIOR TO STARTING CONSTRUCTION. CONTRACTOR SHALL BE RESPONSIBLE FOR REPAIRING EXISTING ITEMS DAMAGED DURING CONSTRUCTION, SUCH AS, BUT NOT LIMITED TO, DRAINAGE, UTILITIES, PAVEMENT, STRIPING, CURB, ETC. DAMAGES SHALL BE REPORTED TO ENGINEER OF RECORD PRIOR TO REPAIR. REPAIRS SHALL BE EQUAL TO, OR BETTER THAN, EXISTING CONDITIONS.
- PROPOSED CONSTRUCTION ON THIS SITE SHALL COMPLY WITH THE LATEST REVISION OF THE ADA REGULATIONS AND THE TEXAS ACCESSIBILITY STANDARDS (TAS).
- EROSION AND SEDIMENTATION CONTROL DURING CONSTRUCTION SHALL BE IN COMPLIANCE WITH LOCAL AND STATE REQUIREMENTS.
- CONTRACTOR SHALL BE RESPONSIBLE FOR MAINTAINING PROPER DRAINAGE THROUGHOUT THE SITE DURING CONSTRUCTION. CARE SHALL BE TAKEN TO PREVENT ANY NEGATIVE IMPACTS TO ADJACENT PROPERTIES.
- CONTRACTOR SHALL CAREFULLY MONITOR WEATHER PATTERNS AND PREPARE FOR EXPECTED EVENTS. SPECIAL CARE SHALL BE TAKEN TO EXAMINE SITE PRIOR TO WEEKENDS OR ABSENCES FROM THE WORKSITE.
- NO HAZARDOUS MATERIALS WERE IDENTIFIED DURING PRELIMINARY SITE INVESTIGATIONS. ANY ITEMS FOUND SUSPECT DURING CONSTRUCTION SHOULD BE BROUGHT TO THE ATTENTION OF THE ENGINEER IMMEDIATELY.

PARKING REQUIREMENT CAHRT

UNIT COUNT	PARKING CALCULATION	PARKING REQUIRED	PARKING PROVIDED
326	1.5 SPACES PER UNIT	189	189
72	2.0 SPACES PER UNIT	144	144
18	2.5 SPACES PER UNIT	45	45
210 TOTAL UNITS	+10% GUEST SPACES	38	9
	TOTAL SPACES	416	387

*29 SHARED SPACES EXIST BETWEEN COMMERCIAL PARCEL AND RESIDENTIAL TO MEET PARKING REQUIREMENTS

FIRE LANE STRIPING NOTE

LOCATION OF FIRE LANE STRIPING SHALL BE APPROVED BY THE LOCAL FIRE MARSHAL. PRIOR TO APPLICATION, UNLESS OTHERWISE DIRECTED BY THE FIRE MARSHAL, FIRE LANE STRIPING SHALL BE 6" RED PAINTED STRIPE ALONG TOP AND FACE OF CURB, FACE OF SIDEWALK, OR DIRECTLY ADJACENT TO PROPOSED PARKING LOT STRIPE WITH 4" WHITE STENCILED LETTERS "FIRE LANE TOW AWAY ZONE" PAINTED ON RED STRIPE AT 30' CENTER TO CENTER MAX SPACING. SEE FIRE LANE STRIPING DETAIL ON C-6.1.

REVISIONS
GMA COMMENT RESPONSE-MAY 2023
ISSUE #6 05/01/23 ADDENDUM #5
CITY COMMENT RESP. & VE ITEMS 07/18/2023

LAS ENTRADAS SOUTH SECTION 4 MANOR
GREGG MANOR ROAD
MANOR, TEXAS

SITE PLAN

ISSUED FOR PERMITTING - 03/03/2023

CARNEY ENGINEERING, PLLC.

5465 LEGACY DRIVE, SUITE 650
PLANO, TEXAS 75024
PH (469) 443-0861
FAX (469) 443-0863

TYPE FIRM REGISTRATION NO. F-6033

DRAWN BY: BGH
CHECKED BY: BFB
START DATE: 08/17/2022
SCALE: SEE PLAN
PROJECT NO.: 2008-220